



外壁サイディング表記: □はベース、目はアクセント


No.	メーカー	ベース (品番)	ベース (カラー)	アクセント (品番)	アクセント (カラー)	玄関	サッシ	土台水切り	出隅
25008	KMEW (一般地域用)	レナータストーン	QWJルシールブラック	パストラル	QWニュアンスベージュ	ブラック	ブラック	ブラック	ブラック

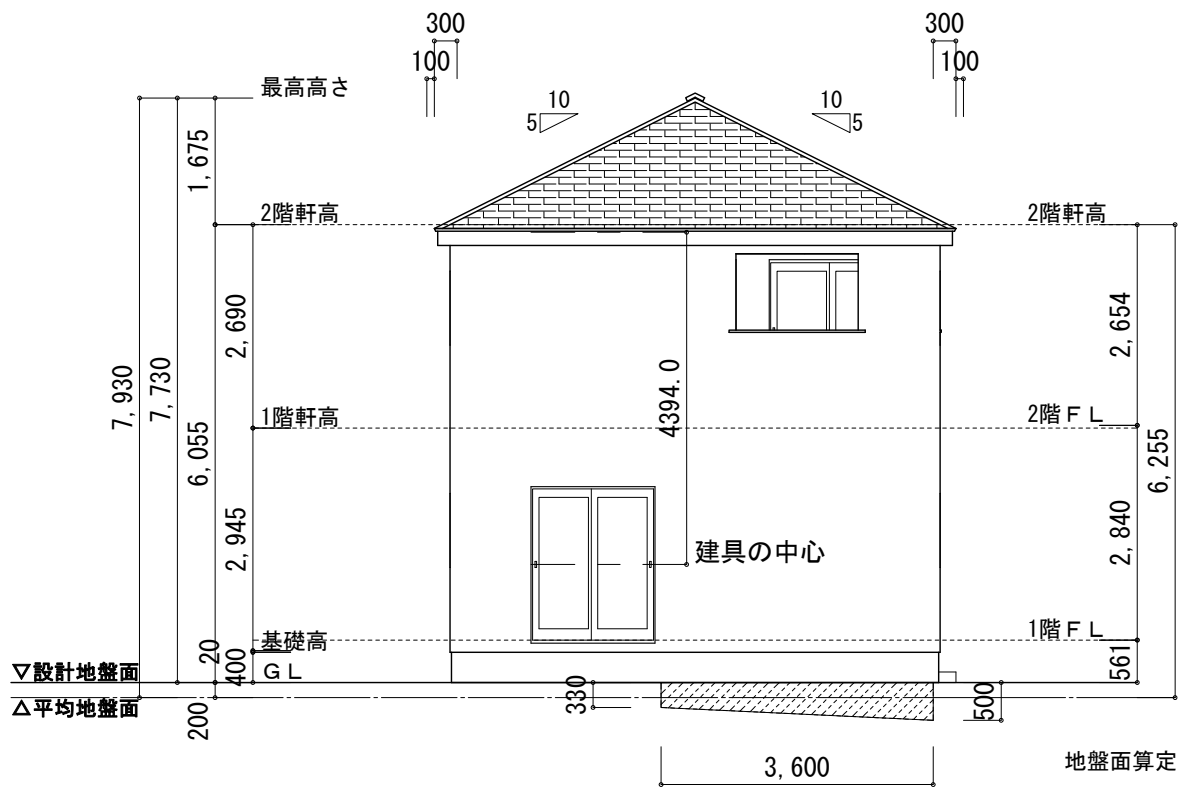


南側 立面図 S:1/100

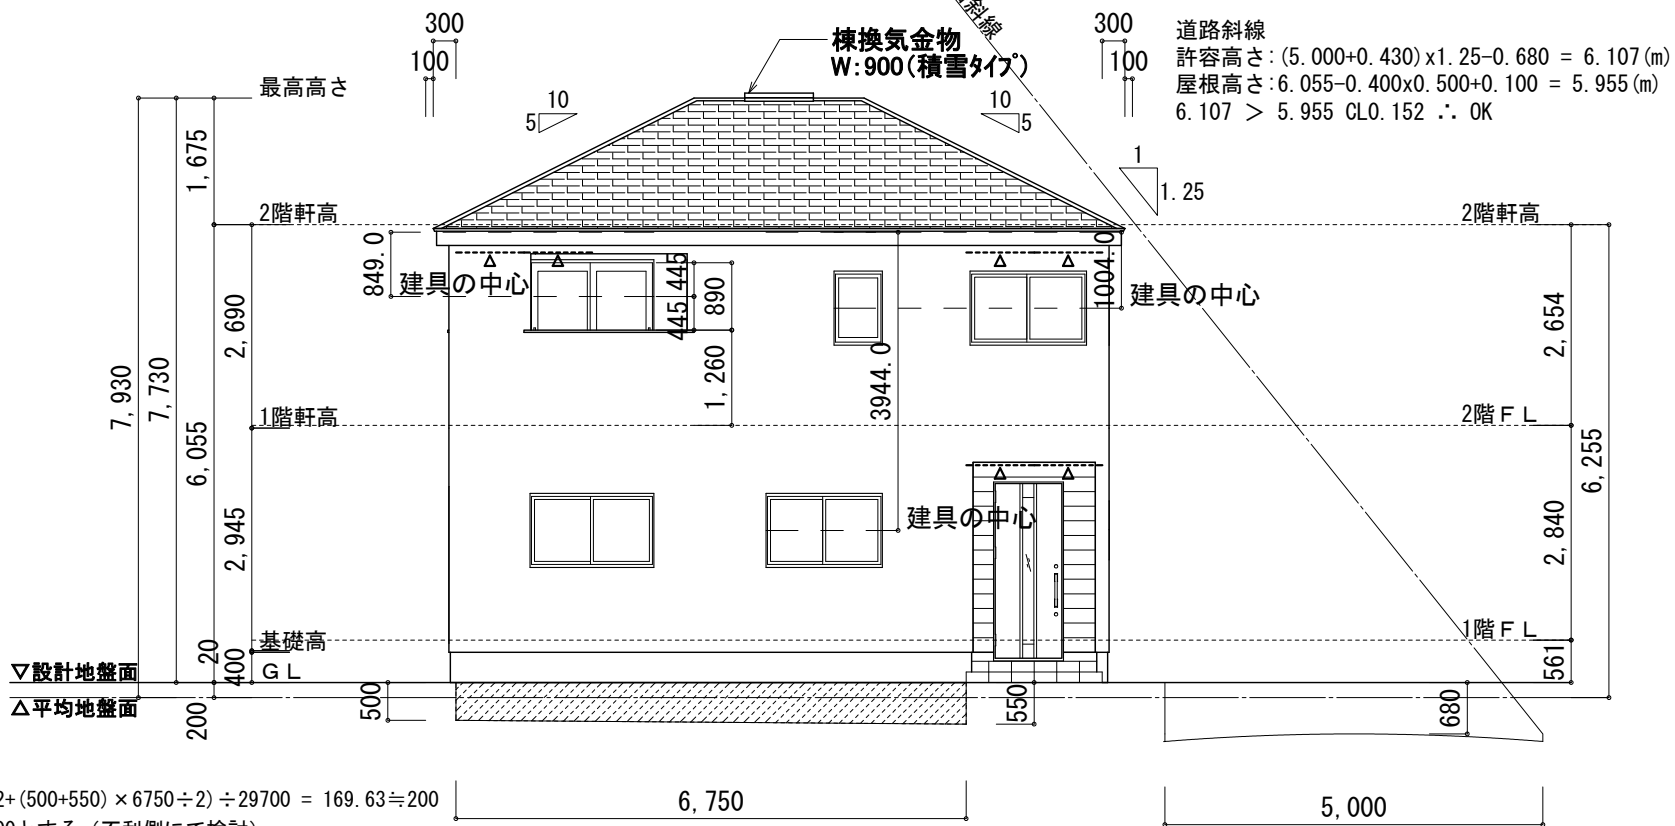



東側 立面図 S:1/100

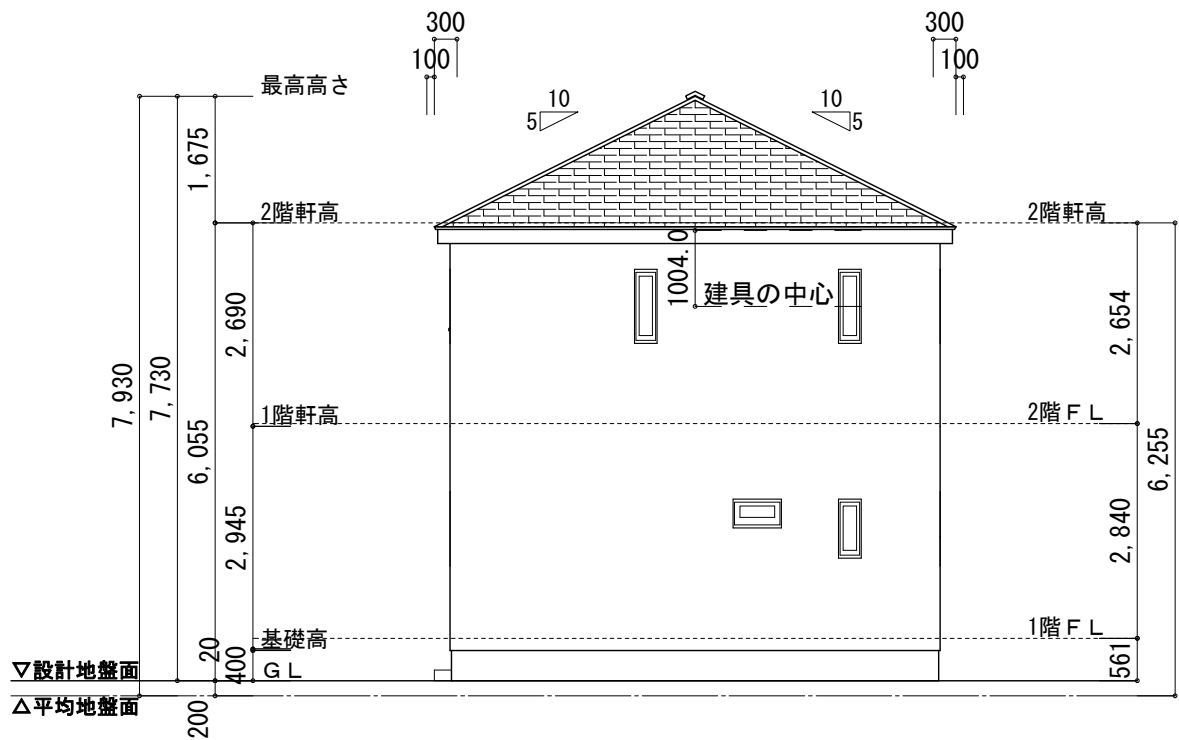

北側 立面図 S:1/100

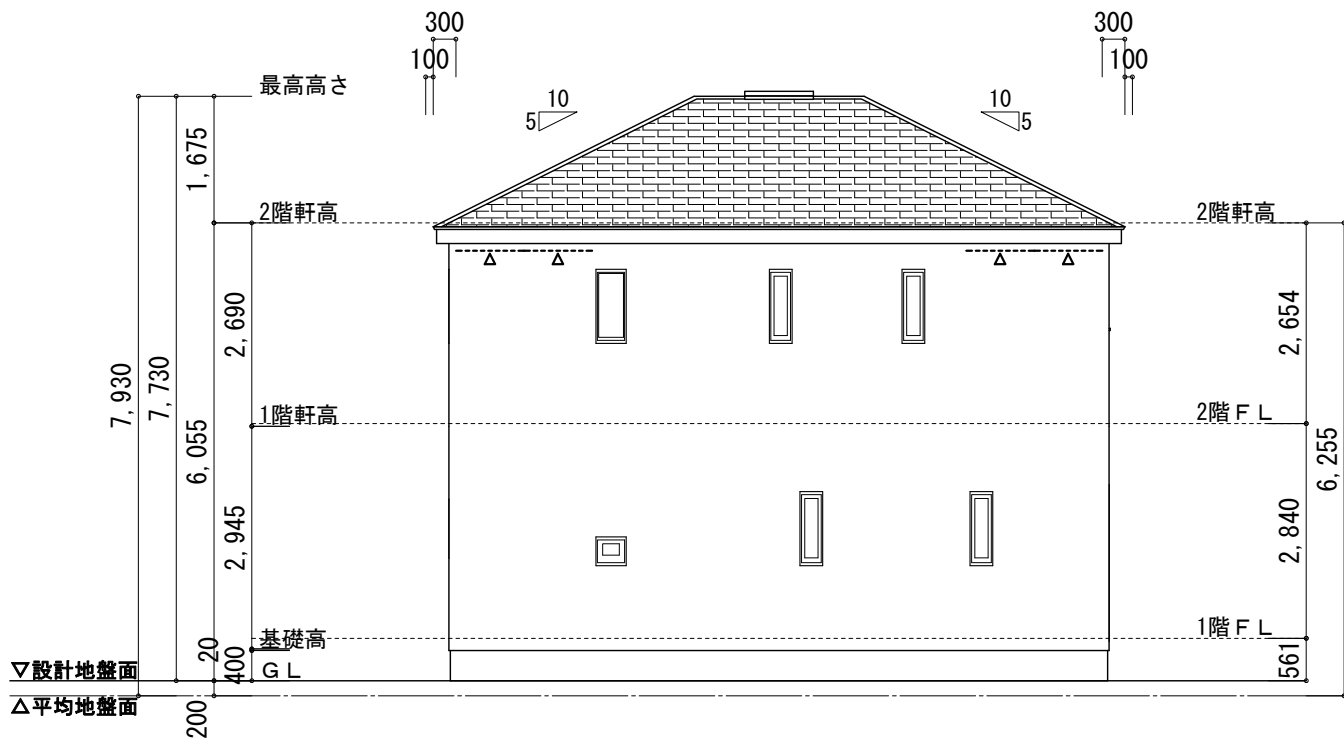

西側 立面図 S:1/100

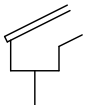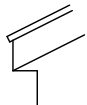変更及特記事項	軒先形状は下記いずれかとする	特記事項	飯田グループホールディングス 株式会社アーネストワン	原図	下川 (石澤)	千葉	工事名 千葉市中央区川戸町第3(4期2棟)1号棟	図面名 立面図
	 	棟換気金物 (金属板) YY3003BS (1800) 又はYY3102S (900) 又はYY3103S (1800) ※平面図による 軒天通気見切縁 (W=900) 又は軒裏換気金物 (有孔) 4in 9in 鋼板W910) を示す 軒高より上の部分は小屋組みとする ※屋根仕上り厚は100mmとする	検査予約メールアドレス: sekkei-kensayoyaku@arnest1.co.jp 株式会社アーネストワン 一級建築士事務所 東京都知事登録 第44266号 東京都知事登録 第85868号 二級建築士石澤 順三郎		設計担当者	営業区分	22560600100	縮尺 1/100