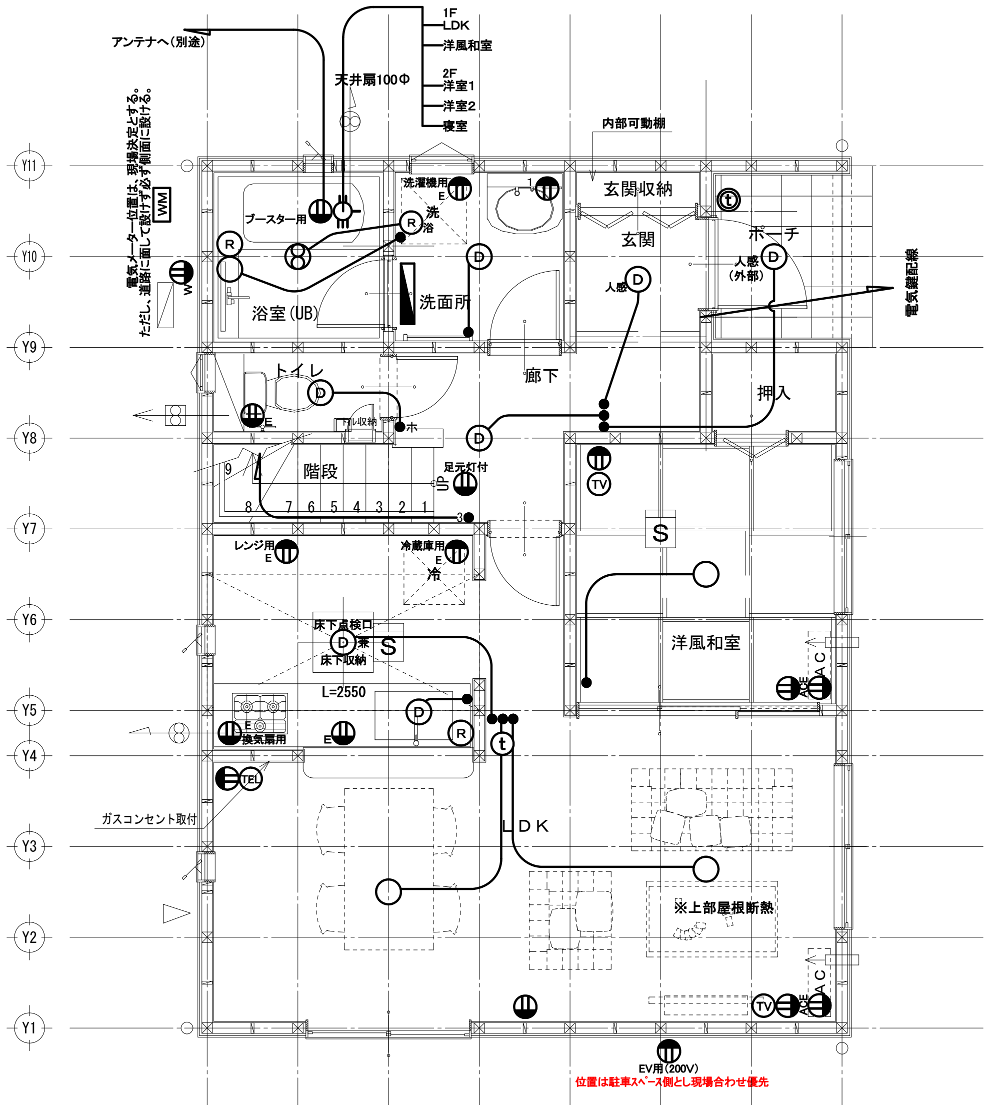

1階　電灯コンセント図　S：1/75

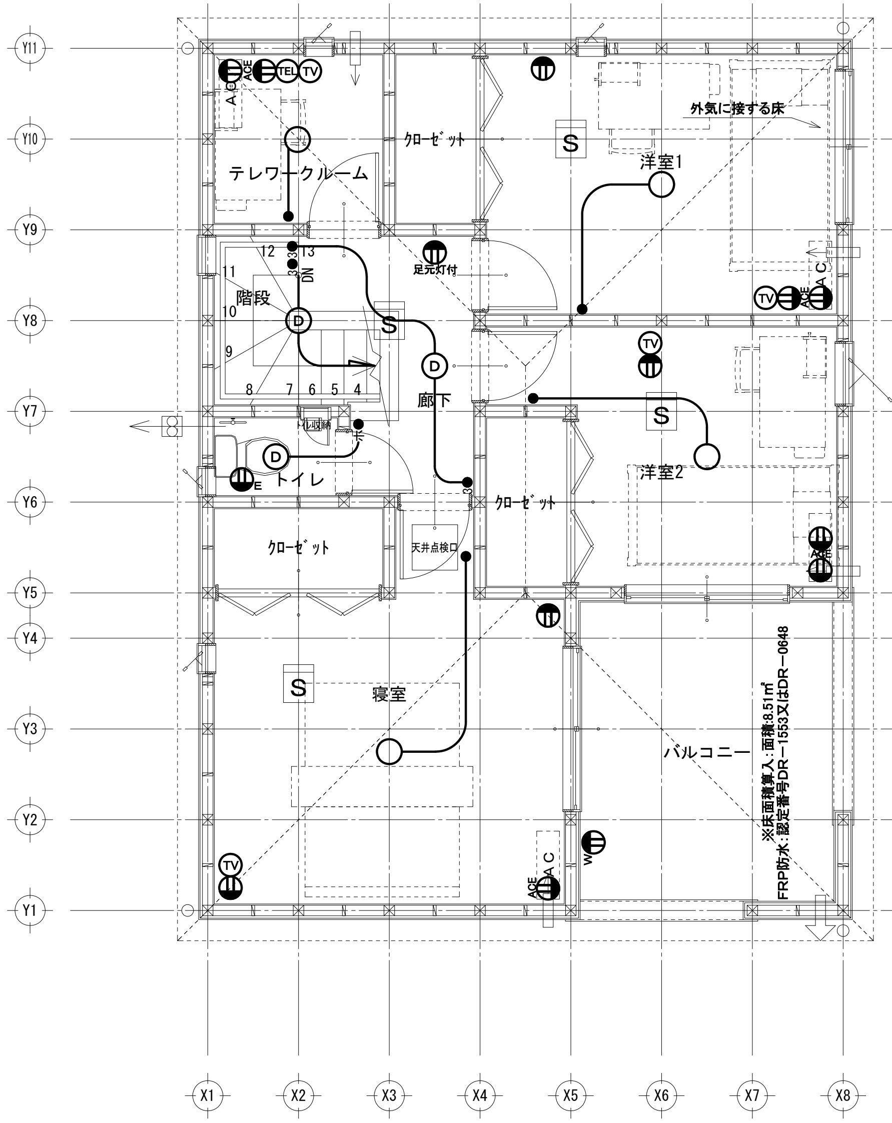

2階　電灯コンセント図　S：1/75

凡　例	
○	引掛シーリング ※勾配天井及び勾配天井に近接する場合、工事マニュアルを優先とする
	天井直付蛍光灯
Ⓓ	天井埋込灯 ※勾配天井及び勾配天井に近接する場合、工事マニュアルを優先とする
	（ダウンライト断熱施工用）
Ⓓ外部	天井埋込灯
	（ダウンライト防雨型）
	手元灯（スイッチ付）
●	スイッチ
●3	3路スイッチ
●ホ	ホタルスイッチ
◎	人感センサー
1	1口コンセント
	2口コンセント
E	アース付2口 コンセント：トイレ、ｷｯﾁﾝ流し前
足元灯	足元灯付 コンセント
E 洗濯機用	
E 冷蔵庫用	アース付2口 コンセント
E レンジ用	アース付2口 コンセント
W	防水2口コンセント
ACE	エアコン用コンセント （アース付）
ⓣ	インターホン（外部）
ⓣ	インターホン （内部テレビ付）
Ⓡ	給湯器用リモコン
Ⓡ浴	浴室乾燥機リモコン
(tel)	電話（空配管）
(TV)	テレビ
	テレビ分配器
	換気扇
	分電盤（14+6回路） ※テレワークルームある場合は空きスペースを使用
WM	積算電力計
	シックハウス対応用換気扇
S	煙式警報機
	熱式警報機

特記

照明ｽｲｯﾁ高：FL+1200

但し、ﾀｵﾙ掛と干渉する

照明ｽｲｯﾁ高FL+1400

1階階段手摺と干渉する場合FL+1400

ｺﾝｾﾝﾄ・TEL・TVﾌﾟﾚｰﾄ高　FL+250

洗濯機用防水ｺﾝｾﾝﾄ高　FL+1200

冷蔵庫用ｺﾝｾﾝﾄ高　FL+1900

ﾚﾝｼﾞ用ｺﾝｾﾝﾄ高　FL+1200

給湯器ｺﾝﾄﾛｰﾗｰ及浴乾ｽｲｯﾁ高　FL+1400

ｲﾝﾀｰﾌｫﾝ親機高　FL+1450

ACｺﾝｾﾝﾄ高 ： FL+1900
※2階はFL+1850
※3階はFL+1800

（半母屋下 ： FL+1650）

（母屋下 ： FL+1400）

ﾄﾞｱﾌｫﾝ ： ﾊﾝｽﾞﾌﾘｰﾃﾚﾋﾞﾄﾞｱﾌｫﾝ

ｽｲｯﾁ ： ﾜｲﾄﾞｽｲｯﾁ

火災警報機取付位置

引掛けｼｰﾘﾝｸﾞより500以上

ｽｲｯﾁ・ｺﾝｾﾝﾄ等の高さは

全てﾌﾟﾚｰﾄ芯

器具取付位置等は

状況により変更する場合あり

防犯カメラ設置位置は現場決定とする。

門柱設置時、インターフォン位置は門柱に合わせ現場決定優先とする。外部外灯配線についても、門柱有無を判断し施工する事。

変更及特記事項

LDK、和洋室、寝室TVコンセントはジャック付、その他の部屋のTVコンセントは配線済ジャック無しとする。

飯田グループホールディングス
株式会社アーネストワン

検査予約ﾒｰﾙｱﾄﾞﾚｽ：sekkei-kensayoyaku@arnest1.co.jp

株式会社アーネストワン一級建築士事務所　東京都知事登録　第44266号

東京都知事登録　第85868号　二級建築士石澤　順三郎

原　図	下　川 （石澤）	千葉	工事名 千葉市中央区川戸町第3(4期2棟)1号棟	図面名 電灯コンセント図 FP:AS南855630－11※桜認定
	設計担当者	営業区分	22560600100	縮尺　1/75